



PLANTA DE SITUAÇÃO

ESCALA 1:500

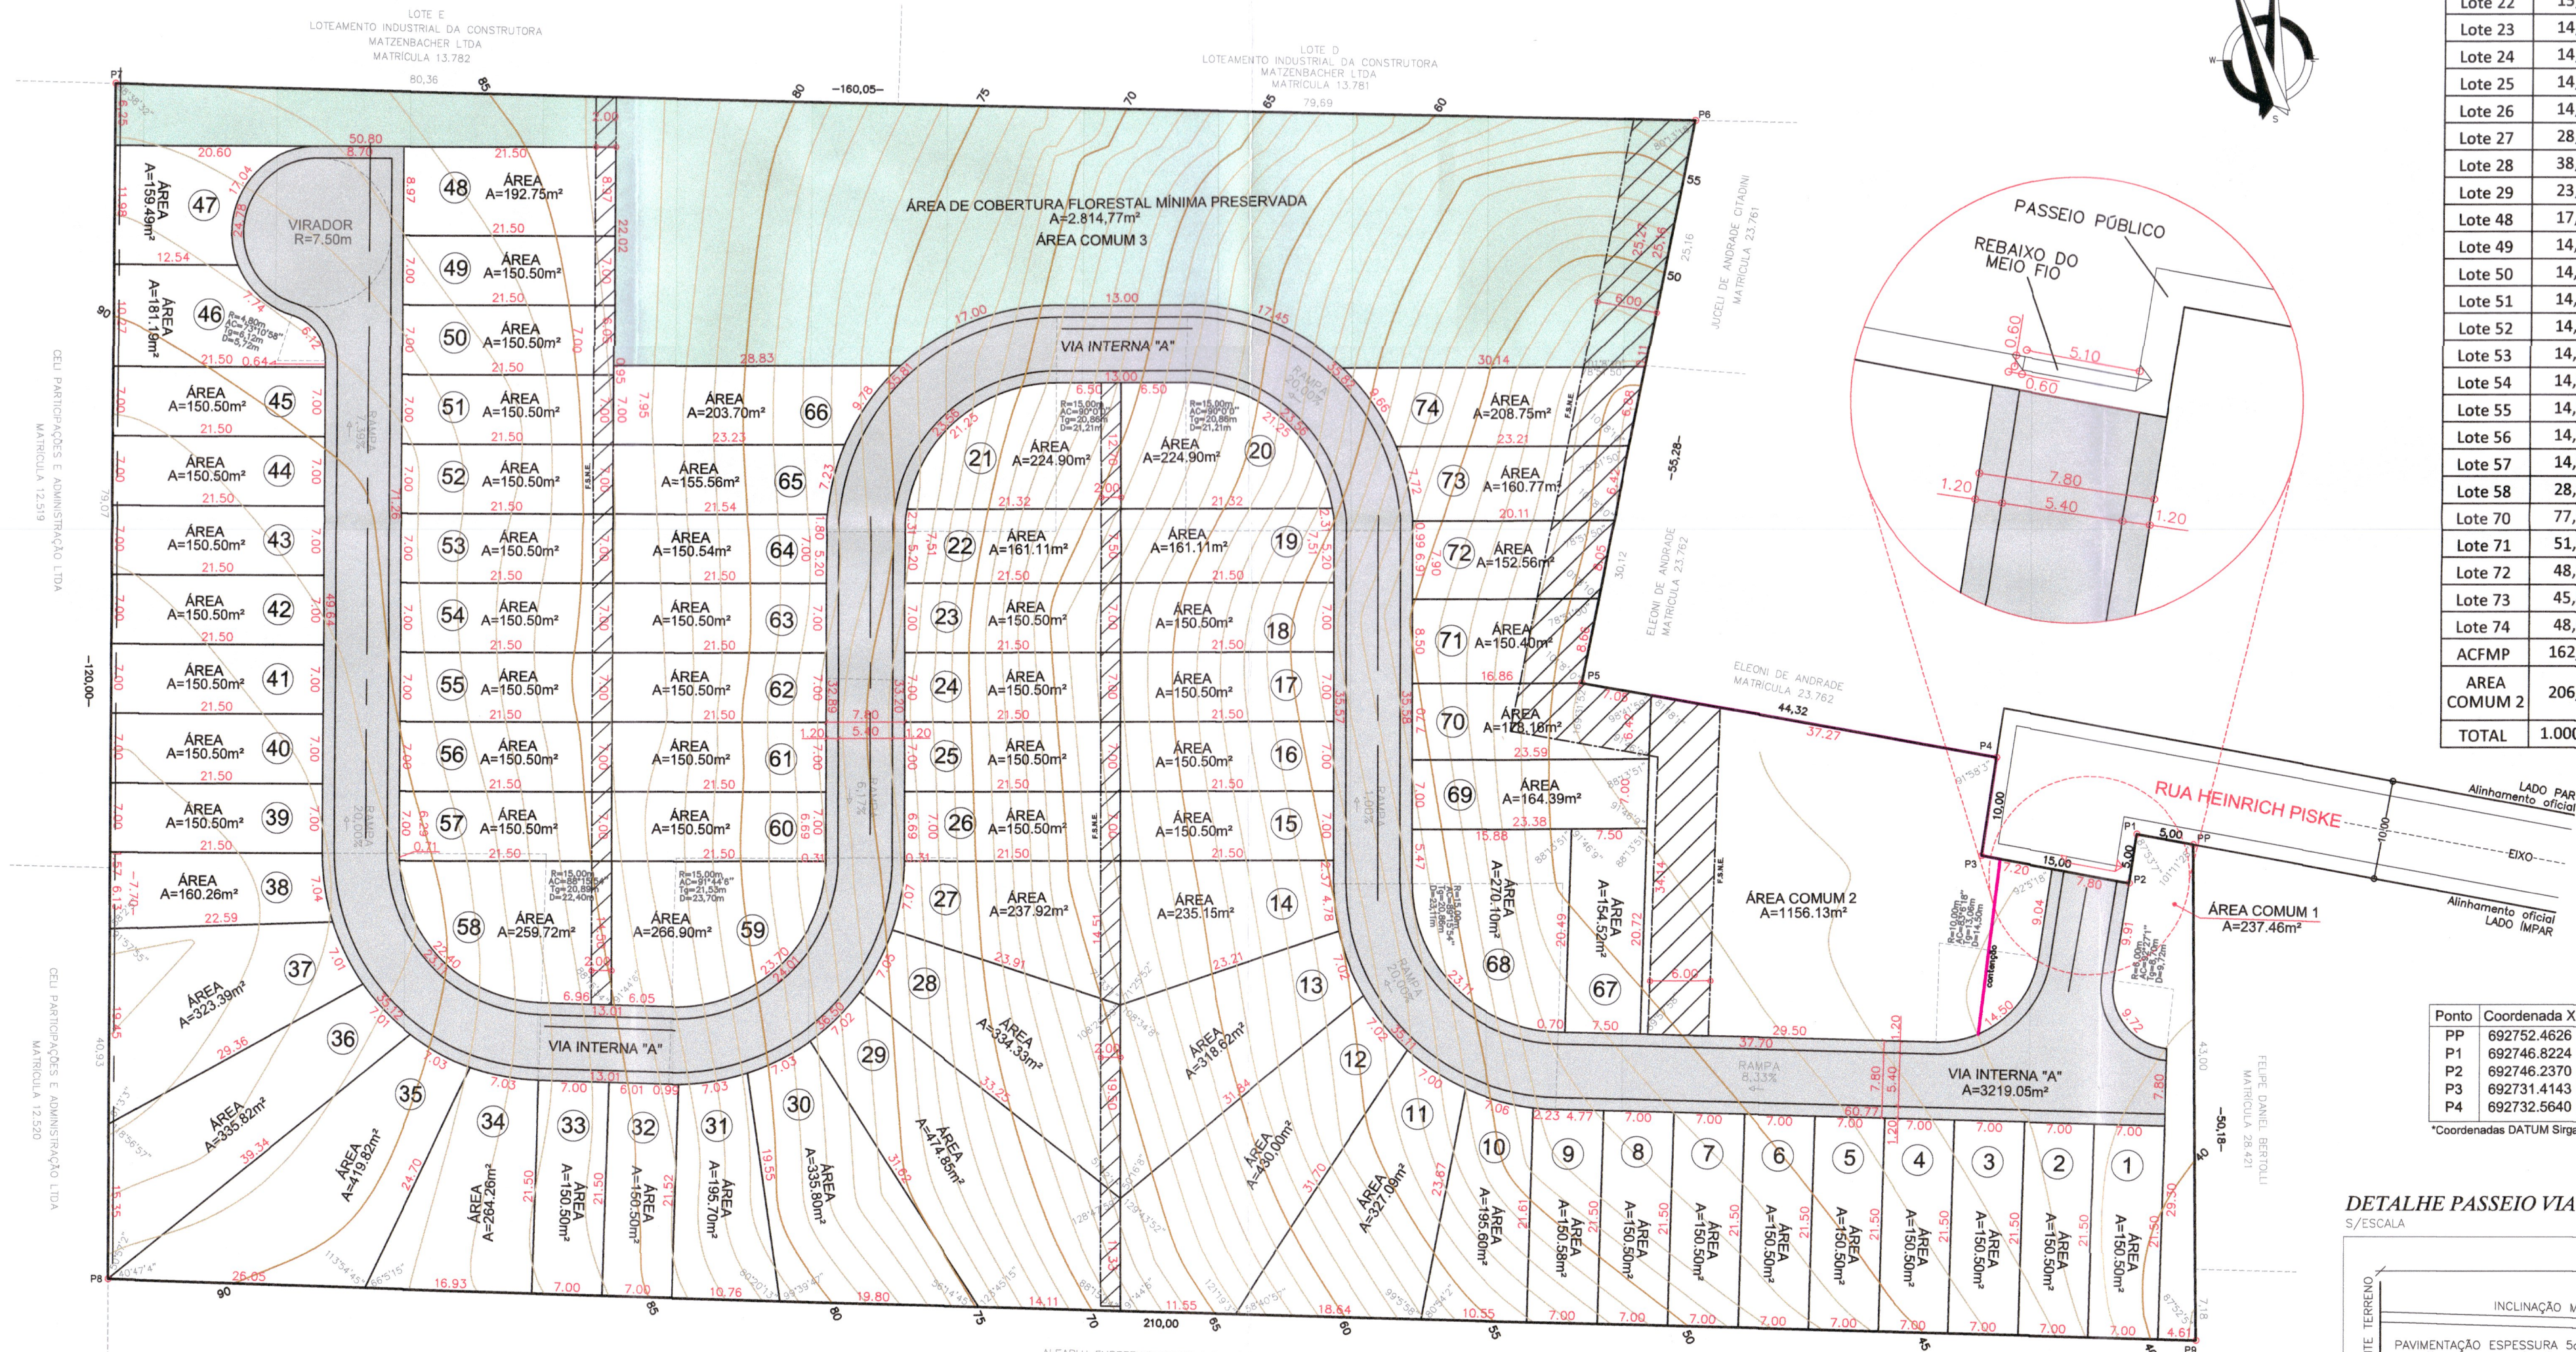


PERFIL LONGITUDINAL VIA INTERNA "A"

ESCALA 1:1250

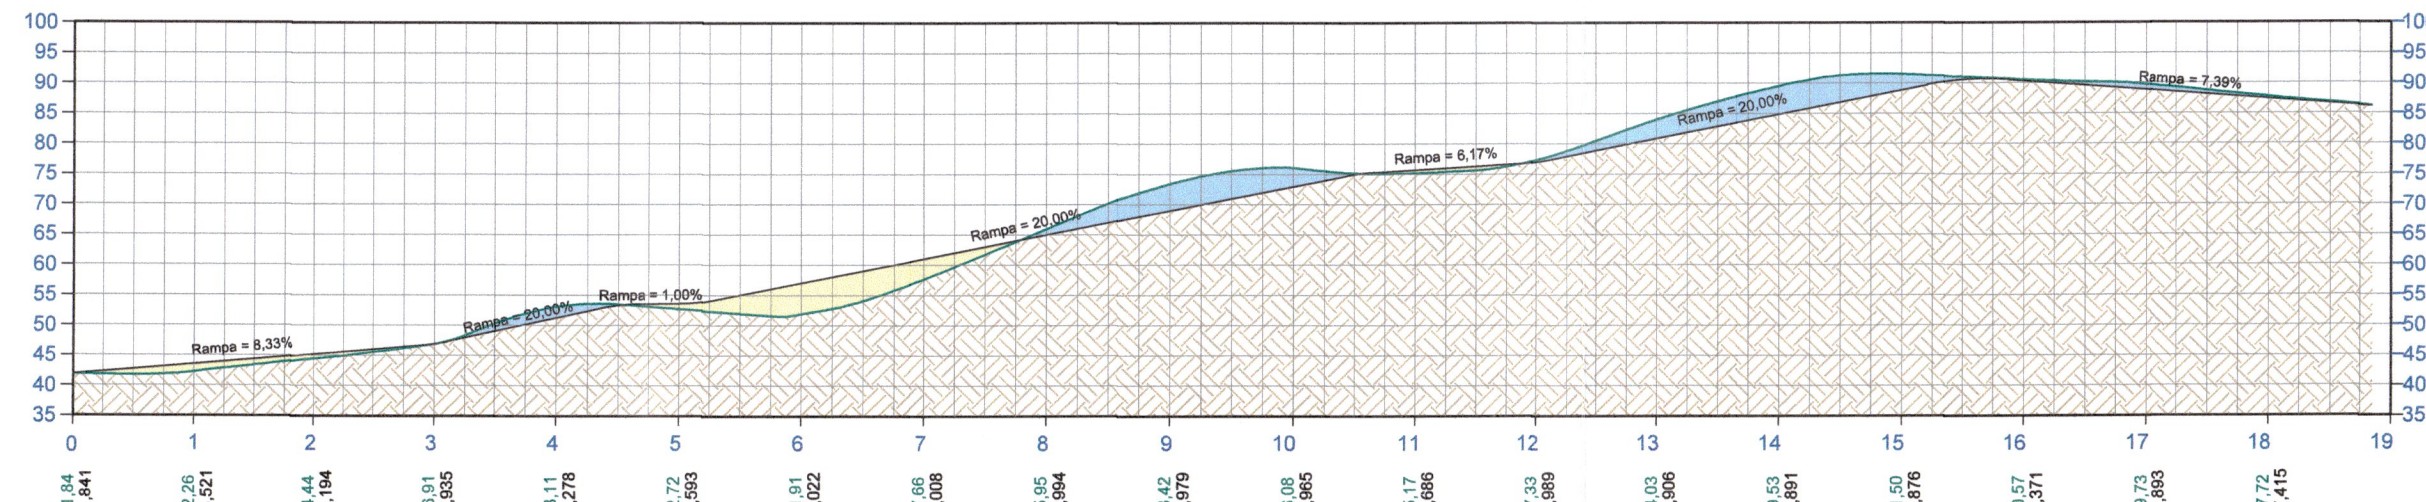


GABARITO VIA INTERNA

S/ESCALA

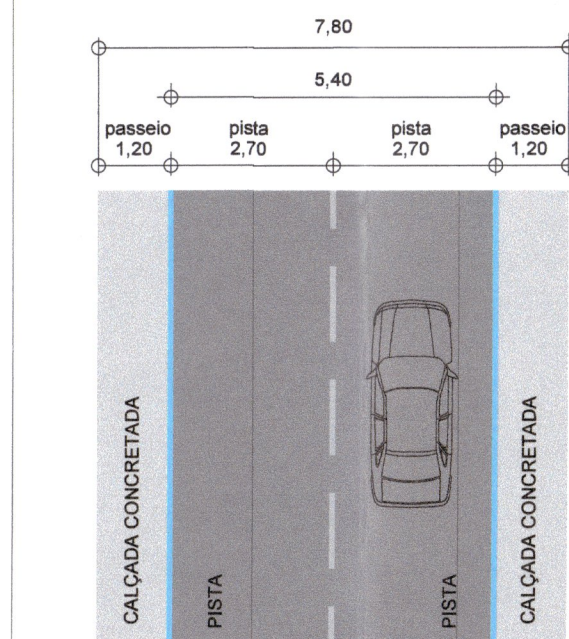


DETALHE PASSEIO VIA INTERNA

S/ESCALA

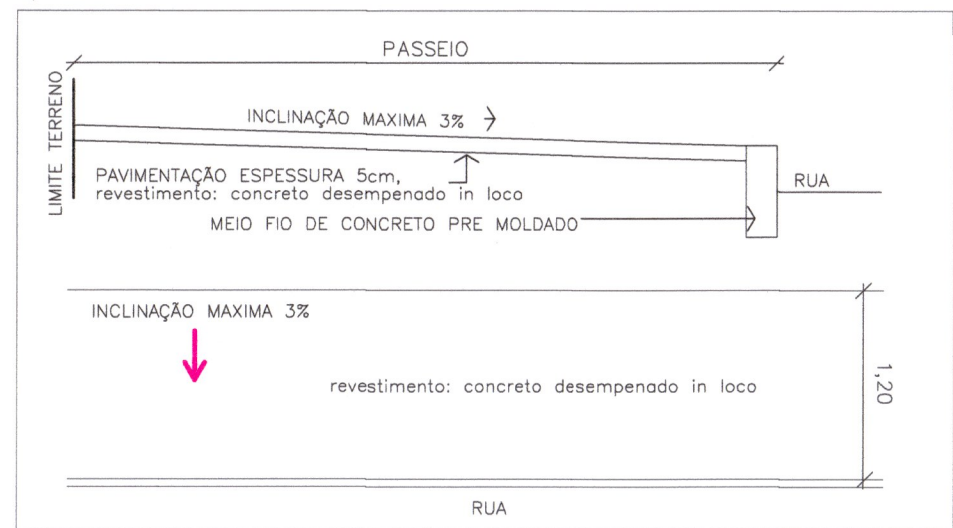

PERFIL LONGITUDINAL VIA INTERNA

S/ESCALA

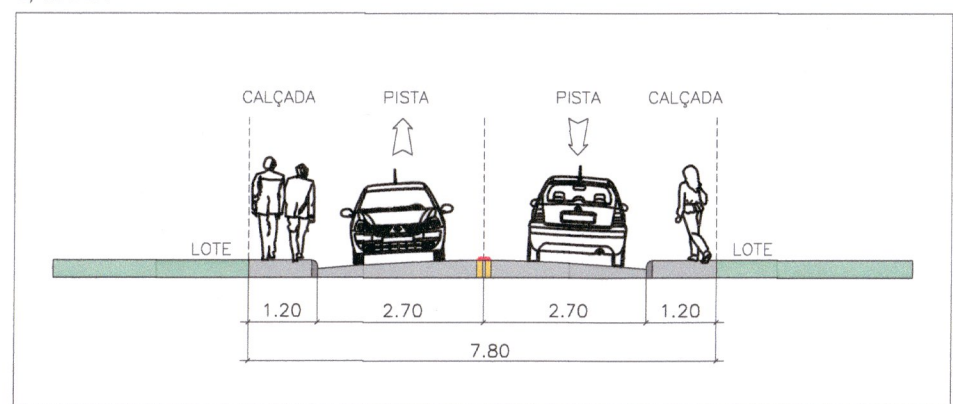

QUADRO RESUMO F.S.N.E

F.S.N.E	ÁREA (m²)
Lote 21	25,40
Lote 22	15,00
Lote 23	14,00
Lote 24	14,00
Lote 25	14,00
Lote 26	14,00
Lote 27	28,35
Lote 28	38,06
Lote 29	23,29
Lote 48	17,93
Lote 49	14,00
Lote 50	14,00
Lote 51	14,00
Lote 52	14,00
Lote 53	14,00
Lote 54	14,00
Lote 55	14,00
Lote 56	14,00
Lote 57	14,00
Lote 58	28,94
Lote 70	77,92
Lote 71	51,97
Lote 72	48,31
Lote 73	45,86
Lote 74	48,61
ACFMP	162,17
ÁREA COMUM 2	206,64
TOTAL	1.000,45

QUADRO RESUMO DE LOTES

LOTE	ÁREA (m²)	LOTE	ÁREA (m²)
Lote 01	150,50	Lote 38	160,26
Lote 02	150,50	Lote 39	150,50
Lote 03	150,50	Lote 40	150,50
Lote 04	150,50	Lote 41	150,50
Lote 05	150,50	Lote 42	150,50
Lote 06	150,50	Lote 43	150,50
Lote 07	150,50	Lote 44	150,50
Lote 08	150,50	Lote 45	150,50
Lote 09	150,58	Lote 46	181,19
Lote 10	195,60	Lote 47	159,49
Lote 11	327,09	Lote 48	192,75
Lote 12	430,00	Lote 49	150,50
Lote 13	318,62	Lote 50	150,50
Lote 14	235,15	Lote 51	150,50
Lote 15	150,50	Lote 52	150,50
Lote 16	150,50	Lote 53	150,50
Lote 17	150,50	Lote 54	150,50
Lote 18	150,50	Lote 55	150,50
Lote 19	161,11	Lote 56	150,50
Lote 20	224,90	Lote 57	150,50
Lote 21	224,90	Lote 58	259,72
Lote 22	161,11	Lote 59	266,90
Lote 23	150,50	Lote 60	150,50
Lote 24	150,50	Lote 61	150,50
Lote 25	150,50	Lote 62	150,50
Lote 26	150,50	Lote 63	150,50
Lote 27	237,92	Lote 64	150,54
Lote 28	334,33	Lote 65	155,56
Lote 29	474,85	Lote 66	203,70
Lote 30	335,80	Lote 67	154,52
Lote 31	195,70	Lote 68	270,10
Lote 32	150,50	Lote 69	164,39
Lote 33	150,50	Lote 70	178,16
Lote 34	264,26	Lote 71	150,40
Lote 35	419,82	Lote 72	152,56
Lote 36	335,82	Lote 73	160,77
Lote 37	323,39	Lote 74	208,75

Ponto	Coordenada X	Coordenada Y	Ponto	Coordenada X	Coordenada Y
PP	692752.4626	7027352.4000	P5	692691.0021	7027366.8135
P1	692746.8224	7027353.2777	P6	692700.2678	7027423.7938
P2	692746.2370	7027348.3174	P7	692541.32	7027422.29
P3	692731.4143	7027350.6171	P8	692545.3140	7027301.8801
P4	692732.5640	7027360.5508	P9	692754.5078	7027302.4813

*Coordenadas DATUM Sirgas2000

QUADRO RESUMO DO CONDOMÍNIO

ESCRITURA (M. 40580 - 3º OFÍCIO)	21.667,12 m²
ÁREA DO CONDOMÍNIO	100,00% 21.667,12 m²
ÁREA DOS LOTES (1-74)	65,72% 14.239,71 m²
ÁREA COMUM (1+2)	6,44% 1.393,59 m²
ÁREA DE VIA INTERNA ("A")	14,84% 3.219,05 m²
ÁREA DE COBERTURA FLORESTAL MÍNIMA PRESERVADA (ÁREA COMUM 3)	13,00% 2.814,77 m²

OBSERVAÇÕES:

- 1) ÂNGULOS NÃO COTADOS EM PLANTA CONSIDERAR COMO 90°;
- 2) ÁREA PÚBLICA A SER COMPENSADA FINANCEIRAMENTE: 2.235,20 m².

Cálculo da Área Pública (mínima) = (0,54*AL-AC)/2 = (0,54*14.239,71m² - 3.219,05m²)/2 = 2.235,20m²

QUADRO DE ÁREAS DE PROJETO ARQUITETÔNICO DAS ÁREAS COMUNS 1 E 2

QUADRO DE RESUMO

Matrícula: 40580 - 3º Ofício			Bairro: Fortaleza						Inscrição Cadastral: 2-6-13-1-445		
			Área Escriturada: 21.667,12 m²			Área Comuns 1,2,3 + Vias: 7.427,41 m²			Uso: RM - Residencial Multifamiliar		
Zoneamento: ZR1			Área ZR1: 18.256,48 m²			Em ZR1: 5.413,53 m²					
ZR3			Área ZR3: 3.410,64 m²			Em ZR3: 2.013,88 m²					
Índices	ZR1	ZR3	Permitido ZR1 (m2)	Permitido ZR3 (m2)	Existente ZR1 (m2)	Existente ZR3 (m2)	A Construir ZR1 (m2)	A Construir ZR3 (m2)	Total em ZR1 (m2)	Total em ZR3 (m2)	Total (m2)
C.A.:	1,2	3,6	6.559,68	7.257,60	-	-	-	342,66	-	342,66	342,66
T.O.:	60	70	3.279,84	1.411,20	-	-	-	252,03	-	252,03	252,03

Área Permeável Exigida (20%)= 1.496,48 m² Área Permeável de Projeto= 2.814,77 m²

Área de vias considerada como área impermeável.

SEPLAN - SEÇÃO MUN. DE PLANEJ. URBANO

APROVADO

PROC. Nº 2021/1768

DATA 20/10/23

Engº Wagner Figueira de Faria
Gerente de Parcelamento do Solo
SEPLAN

Ricardo Michel Gripa
Engº Civil
Matr. 230068 SEPLAN

QUADRO DE ÁREAS DE PROJETO ARQUITETÔNICO DAS ÁREAS COMUNS 1 E 2

QUADRO DE ÁREA CONTRUIDAS - ÁREA COMUM

	Computável (m²)	Não Computável (m²)	Total (m²)
Pavto Térreo - Guarita	84,61	0,00	84,61
Pavto Superior - Academia	84,61	0,00	84,61
Salão de Festas	99,96	0,00	99,96
Quiosque	67,46	0,00	67,46
Caixa d'água	6,02	0,00	6,02
TOTAL	342,66	0,00	342,66

SERGIO LUIZ HAYASHI
59774207904

FELIPE RUTHES CORDEIRO DE AQUINO:04918105980

Assinado de forma digital por FELIPE RUTHES CORDEIRO DE AQUINO:04918105980
Dados: 2023.10.19 16:59:29 -03'00'

PROJETO: PROJETO FÍSICO	CLIENTE: VOGAR - BLUMENAU HILL RESIDENCE EMP. IMOB. SPE LTDA
REF.: PROJETO FÍSICO CONDOMÍNIO DE LOTES	LOCAL: RUA HEINRICH PISKE, Nº733 - FORTALEZA - BLUMENAU /SC
RESP. TÉCNICO: SERGIO LUIZ HAYASHI ENG. CIVIL - CREA 10º REG. 35.917-9	DATA: OUTUBRO DE 2023 LEVANTAMENTO: TOPO.dwg
ESCALA: 1 / 500	PRANCHA: DF-02